
# Hall 2 · montagem cotada

2º turno · montagem sáb. 24/10/2026 · votação dom. 25/10

Escala 1:190 em A3 · medidas em metros · ajustes D1–D4 de 23/10

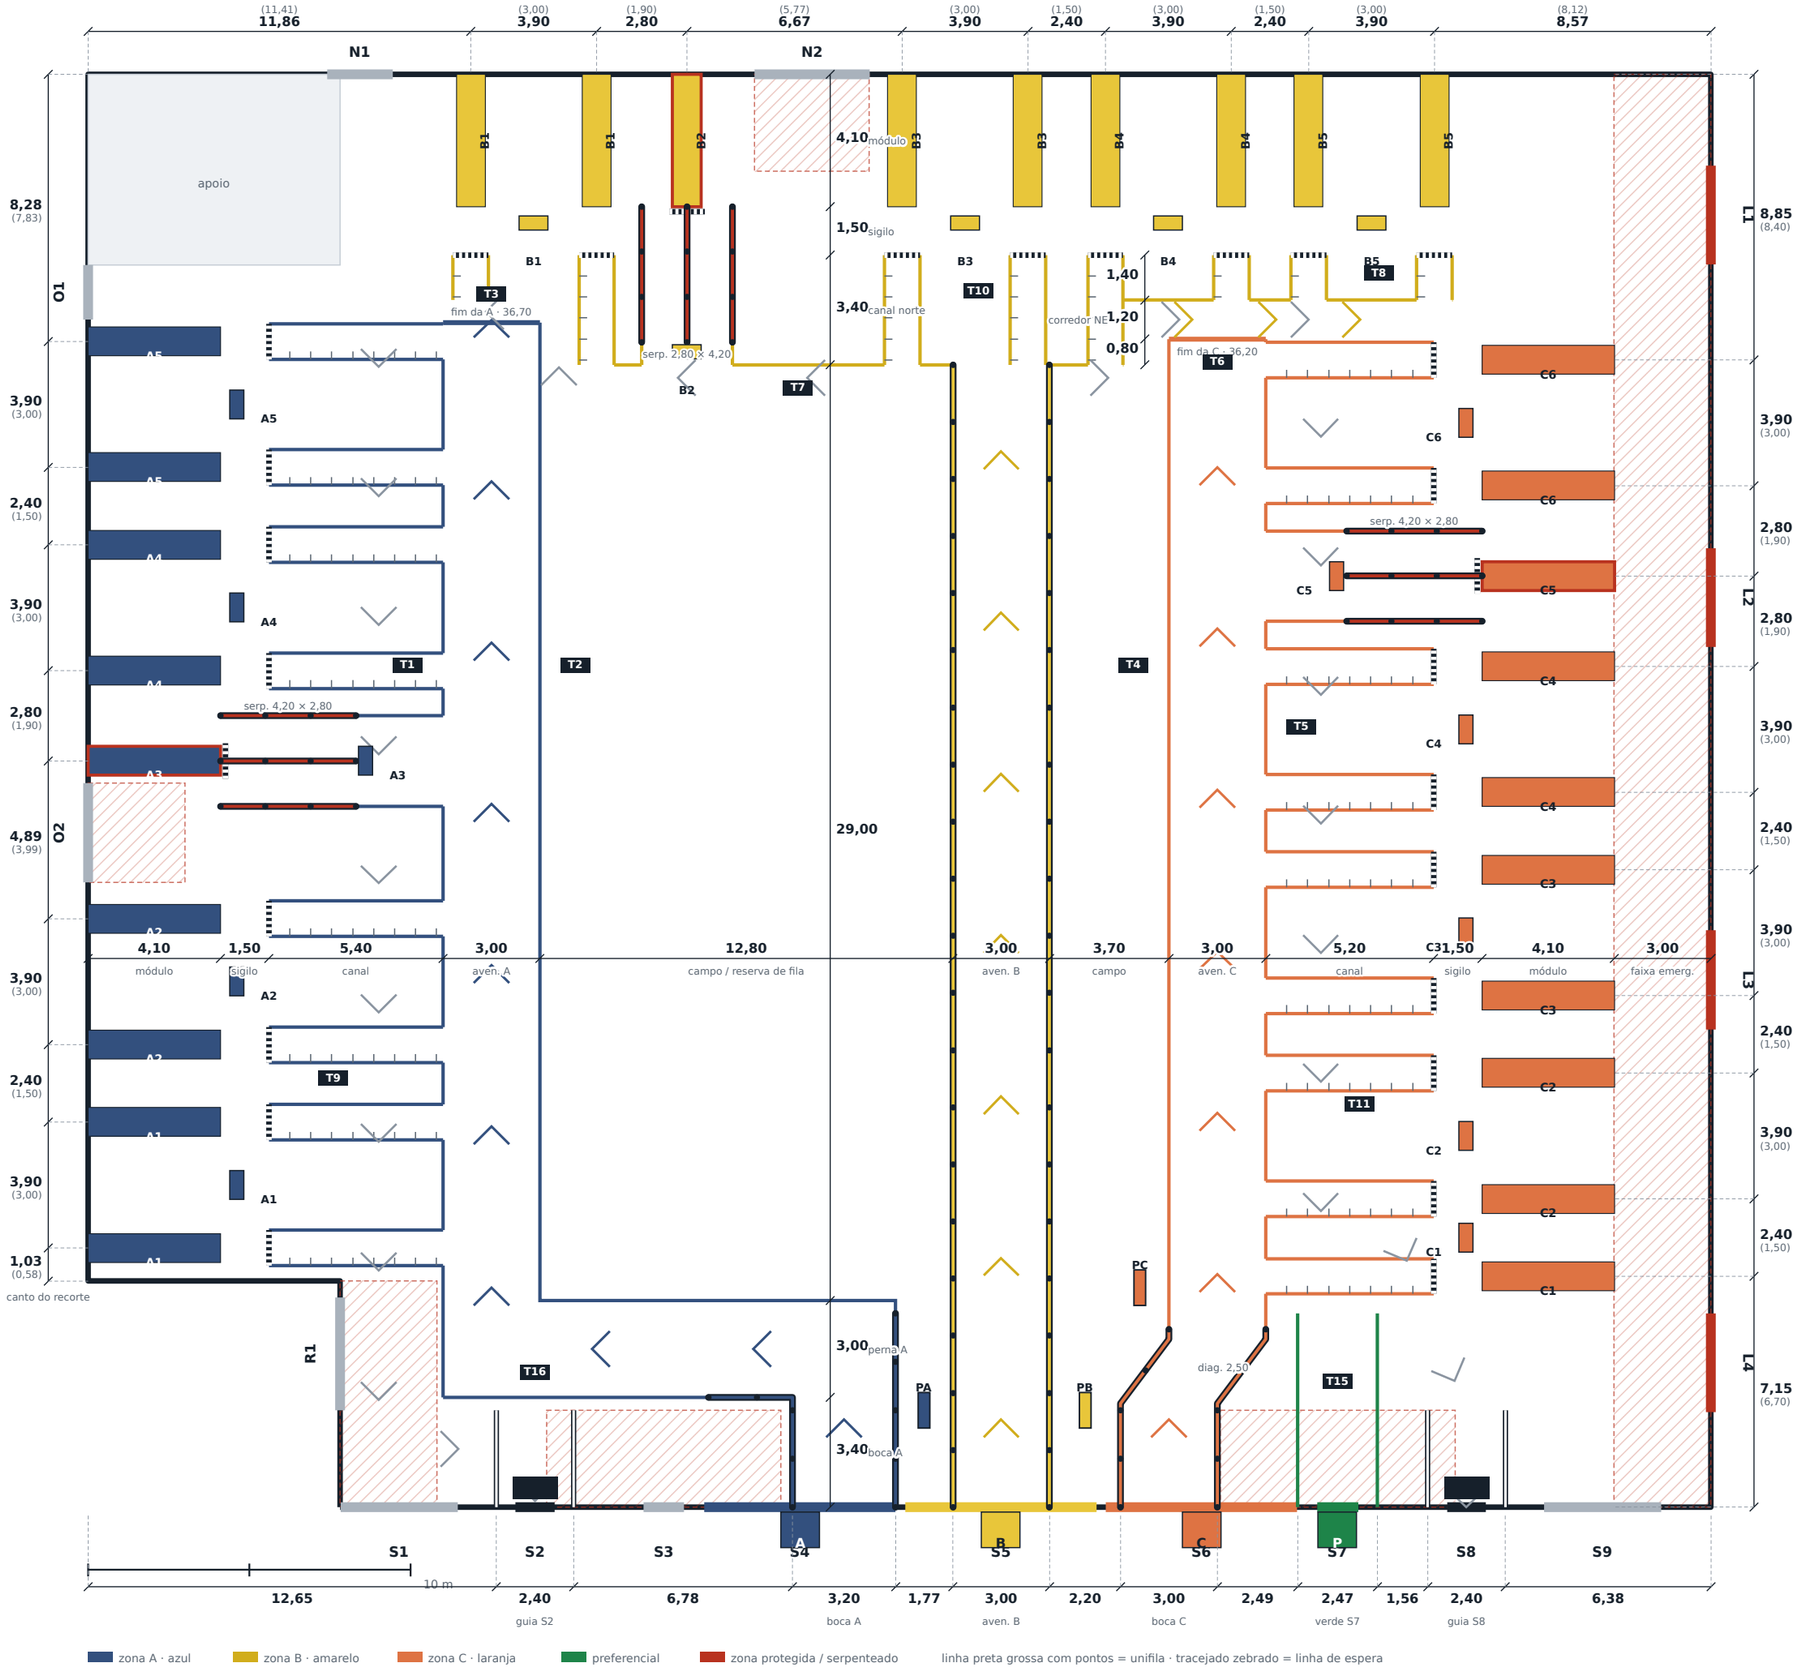


## Fita por trecho

| trecho | | metros |
|---|---|---|
| T1 | Avenida A · linha do lado da parede | 35,9 |
| T2 | Avenida A · linha do lado do campo | 47,7 |
| T3 | Fecho da avenida A | 3,0 |
| T4 | Avenida C · linha do lado do campo | 36,7 |
| T5 | Avenida C · linha do lado da parede | 24,0 |
| T6 | Fecho da avenida C | 3,0 |
| T7 | Distribuidor norte (y 35,40) | 7,8 |
| T8 | Borda do corredor nordeste (y 37,40) | 6,9 |
| T9 | Canais da parede oeste | 91,8 |
| T10 | Canais da parede norte | 39,8 |
| T11 | Canais da parede leste | 98,6 |
| T13 | Marcas de fila (0,25 a cada 0,65) · 64 un | 16,0 |
| T13 | Marcas de fila (0,25 a cada 0,65) · 28 un | 7,0 |
| T13 | Marcas de fila (0,25 a cada 0,65) · 63 un | 15,8 |
| T14 | Galões no eixo · 10 un | 9,0 |
| T14 | Galões no eixo · 10 un | 9,0 |
| T14 | Galões no eixo · 7 un | 6,3 |
| T12 | Linhas de espera · 28 × 1,10 | 30,8 |
| T15 | Canal da preferencial S7 · 2 × 6,00 | 12,0 |
| T16 | Guias de S2 e S8 · 4 × 3,00 | 12,0 |
| T17 | Galões brancos de saída · 28 un | 25,2 |

**Total por cor (com 10% de retoque · rolos de 50 m)**

| | | | |
|---|---|---|---|
| azul | 203,5 m | 223,8 m | **5 rolo(s)** |
| amarelo | 70,5 m | 77,5 m | **2 rolo(s)** |
| laranja | 184,4 m | 202,8 m | **5 rolo(s)** |
| zebrado | 30,8 m | 33,9 m | **1 rolo(s)** |
| verde | 12,0 m | 13,2 m | **1 rolo(s)** |
| branco | 37,2 m | 40,9 m | **1 rolo(s)** |
| **total** | **538 m** | **592 m** | |

## Barreira (unifila · postes a 1,80 m)

| | | |
|---|---|---|
| boca A · 2 cinta(s) de trilho | 12,0 m | **10 postes** |
| boca C · 2 cinta(s) de trilho | 12,0 m | **10 postes** |
| avenida B · 2 cinta(s) de trilho | 70,8 m | **42 postes** |
| serpenteado A3 · 3 cinta(s) de trilho | 12,6 m | **12 postes** |
| serpenteado B2 · 3 cinta(s) de trilho | 12,6 m | **12 postes** |
| serpenteado C5 · 3 cinta(s) de trilho | 12,6 m | **12 postes** |
| **total em uso · reserva 2 (+15 se compradas)** | | **98 postes** |

## Como ler

Cadeias de fora da planta: eixo a eixo das mesas, medido ao longo da parede. Entre parênteses: espaço livre entre módulos (módulo = 0,90 m de largura).
Oeste: medir a partir do canto do recorte (y 7,00).
Leste: as mesas encostam na linha 47,30, a 3,00 m da fachada; a faixa até a fachada fica livre.
Cadeia da fachada sul: medir a partir da parede oeste (x 0) ou do batente de porta mais próximo.
Fita: 50 mm. Tiques de fila a cada 0,65 m no canal.
Etiquetas T1–T11 na planta = linhas da tabela.
Nenhuma peça para o eleitor leva número de mesa.